DRAUFSICHT

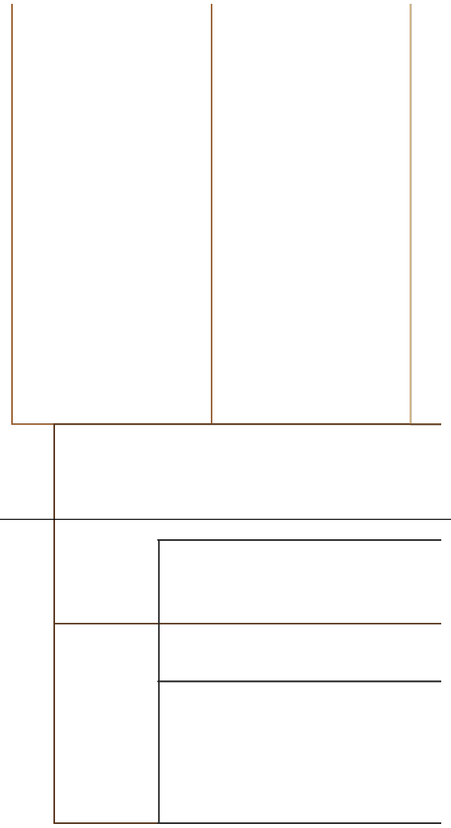

ISOMETRIE

VORDERANSICHT

SEITENANSICHT

MATERIALISTE:

t=8mm:

BackPanel	562x1241=0.697m²
Σ 1 Teile / 0.697m²	

t=19mm:

Bottom	562x560=0.315m²
Top	562x560=0.315m²
LeftSide	560x1279=0.716m²
RightSide	560x1279=0.716m²
Shelf1	562x552=0.310m²
Shelf2	562x552=0.310m²
Shelf3	562x552=0.310m²
Door	596x1275=0.760m²
Σ 8 Teile / 3.752m²	

LEONARD GOEKER Design Projektmanagement

LEONARD GOEKER Design Projektmanagement

B=600 H=1279 T=579 mm Maßstab 1:10