DRAUFSICHT

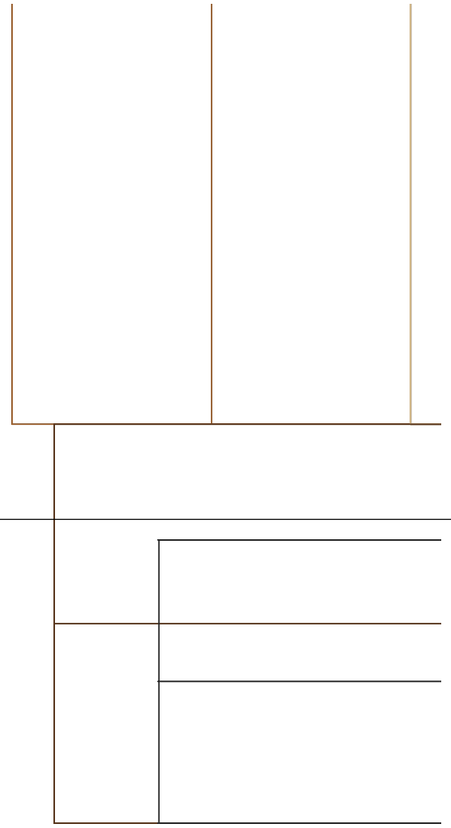

ISOMETRIE

VORDERANSICHT

SEITENANSICHT

MATERIALISTE:

t=8mm:

BackPanel	562x535=0.301m²
Σ 1 Teile / 0.301m²	

t=19mm:

Bottom	562x609=0.342m²
Top	562x609=0.342m²
LeftSide	609x573=0.349m²
RightSide	609x573=0.349m²
Shelf1	562x600=0.337m²
Shelf2	562x600=0.337m²
Shelf3	562x600=0.337m²
Door	596x569=0.339m²
Σ 8 Teile / 2.732m²	

LEONARD GOEKER Design Projektmanagement

LEONARD GOEKER Design Projektmanagement

B=600 H=573 T=628 mm Maßstab 1:10